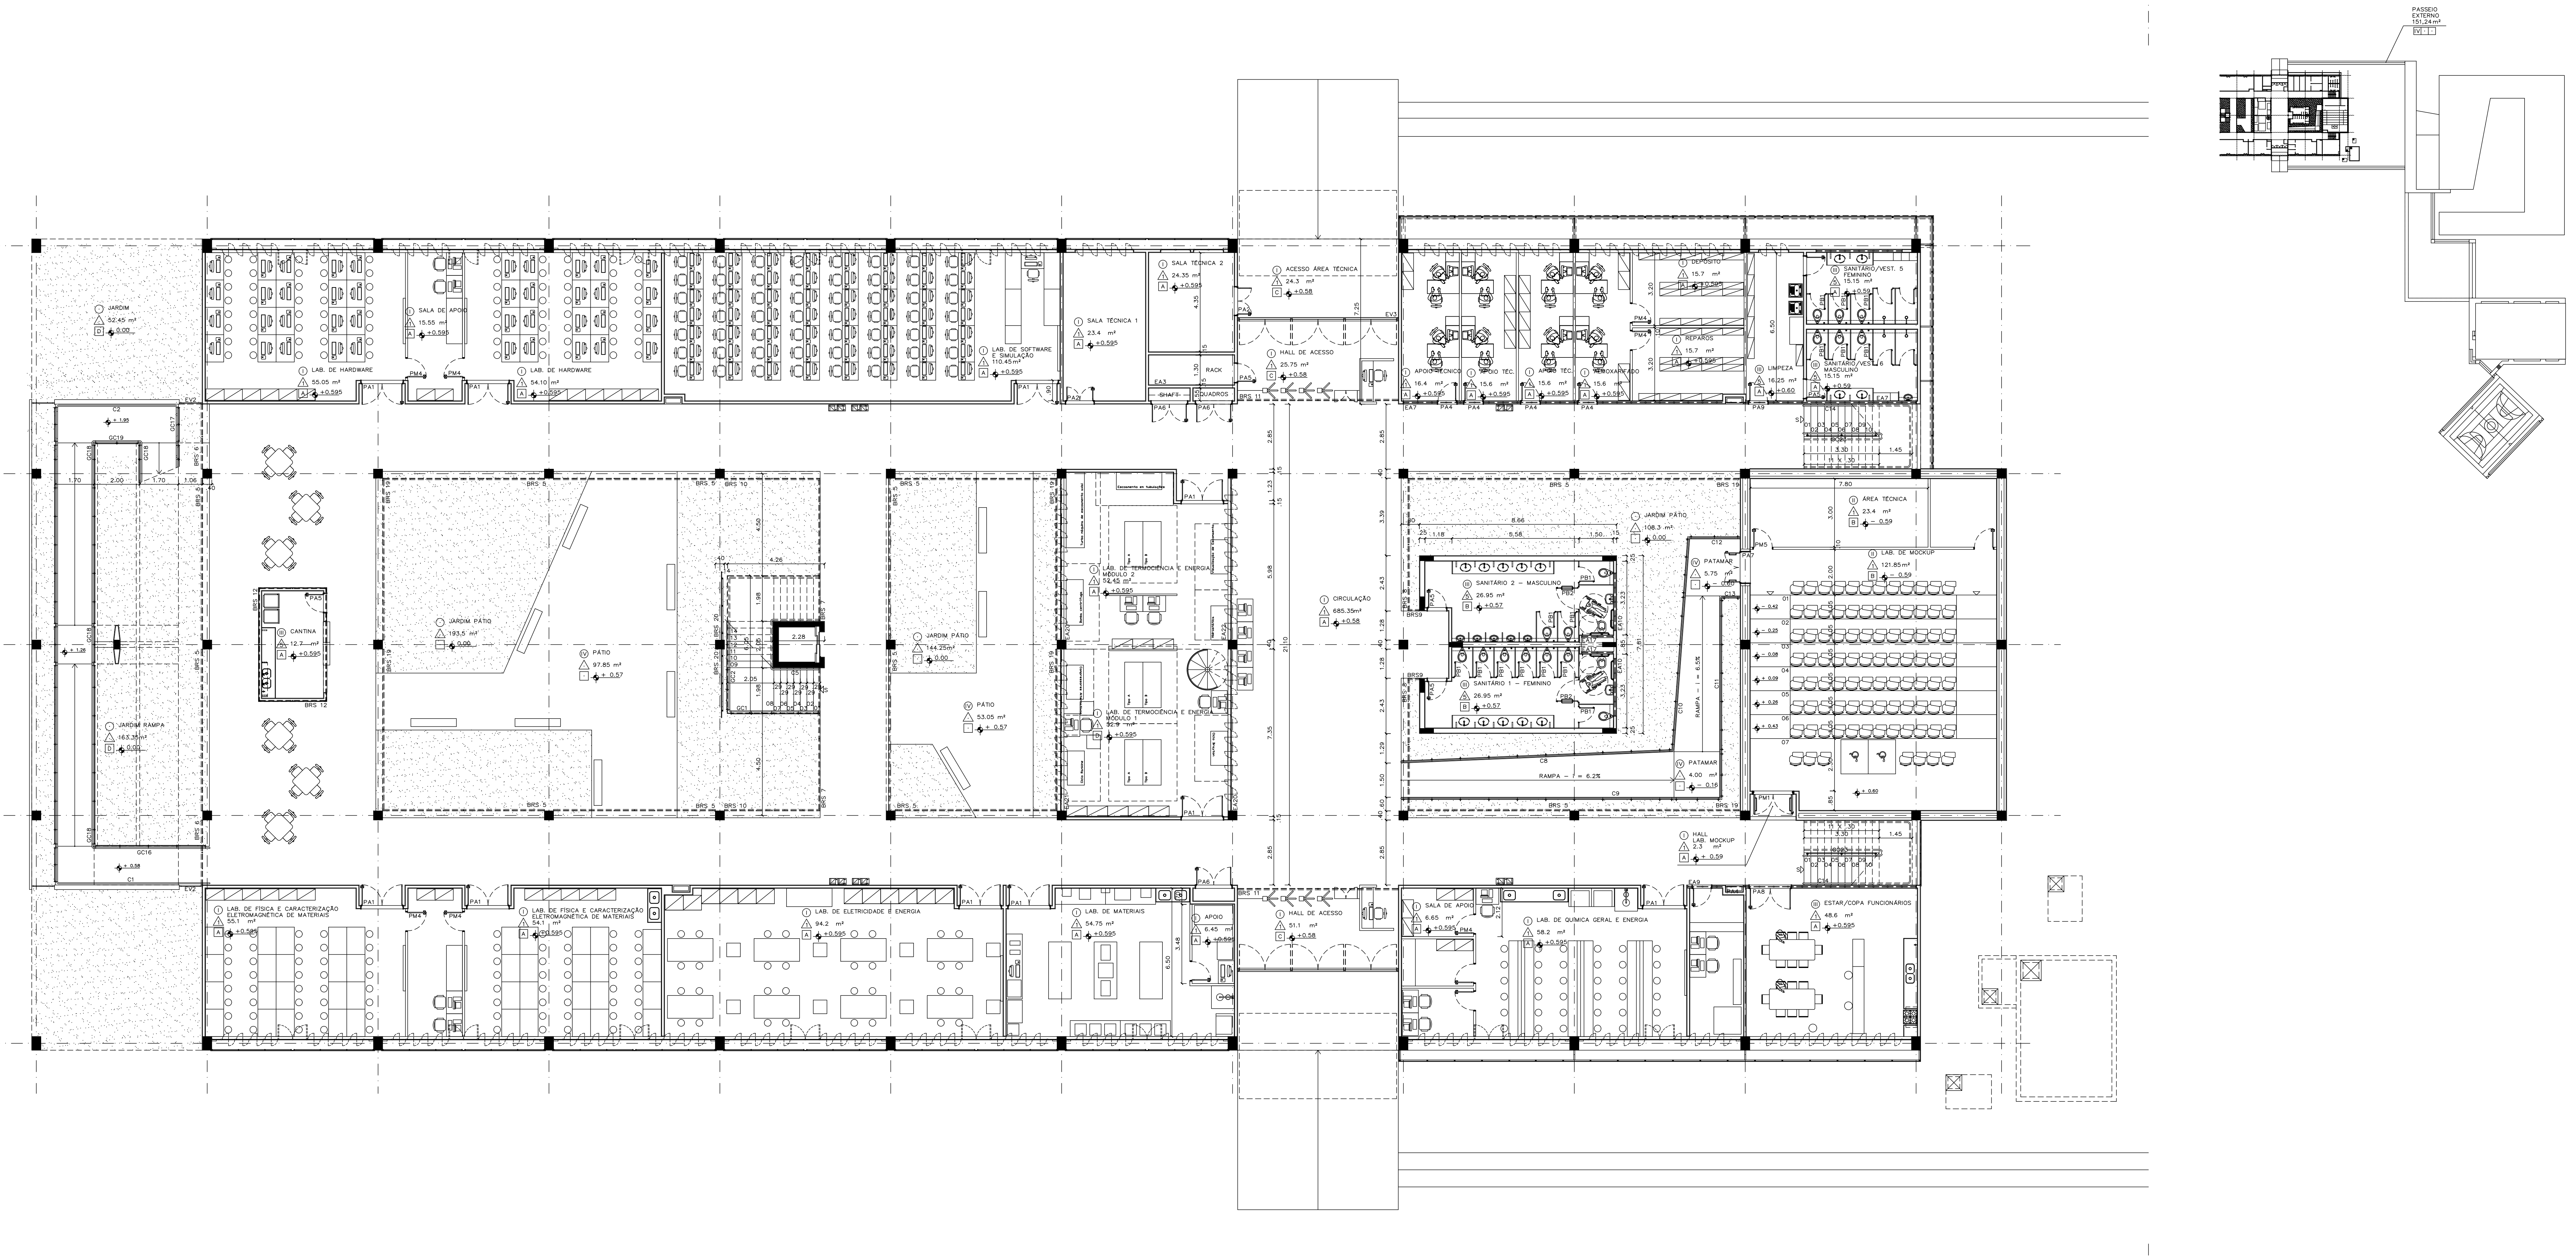
PASSEIO EXTERNO 151,24 m²
JARDIM 52.45 m² 0.00
LAB. DE HARDWARE 55.05 m² +0.595
SALA DE APOIO 15.55 m² +0.595
LAB. DE HARDWARE 54.10 m² +0.595
LAB. DE SOFTWARE E SIMULAÇÃO 110.45 m² +0.595
SALA TÉCNICA 1 23.4 m² +0.595
SALA TÉCNICA 2 24.35 m² +0.595
RACK
SHAFT
QUADROS
ACESSO ÁREA TÉCNICA 24.3 m² +0.58
HALL DE ACESSO 25.75 m² +0.58
APOIO TÉCNICO 16.4 m² +0.595
APOIO TÉC. 15.6 m² +0.595
APOIO TÉC. 15.6 m² +0.595
ALMOXARIFADO 15.6 m² +0.595
DEPOSITO 15.7 m² +0.595
REPAROS 15.7 m² +0.595
LIMPEZA 16.25 m² +0.60
SANITÁRIO/VEST. 5 FEMININO 15.15 m² +0.59
SANITÁRIO/VEST. 6 MASCULINO 15.15 m² +0.59
CANTINA 12.7 m² +0.595
JARDIM PÁTIO 193.5 m² 0.00
PÁTIO 97.85 m² + 0.57
JARDIM RAMPA 163.35m² 0.00
JARDIM PÁTIO 144.25m² 0.00
PÁTIO 53.05 m² + 0.57
LAB. DE TERMOCIÊNCIA E ENERGIA MÓDULO 2 52.45 m² +0.595
LAB. DE TERMOCIÊNCIA E ENERGIA MÓDULO 1 52.9 m² +0.595
Escoamento em tubulações
Turbo máquina de escoamento axial
Bomba centrífuga
Visualização de Escoamento
Hidrostática
Compressores Alternativos
Ciclo Rankine
Ciclo Brayton
Tipo A
Tipo B
CIRCULAÇÃO 685.35m² +0.58
JARDIM PÁTIO 108.3 m² 0.00
SANITÁRIO 2 – MASCULINO 26.95 m² +0.57
SANITÁRIO 1 – FEMININO 26.95 m² +0.57
PATAMAR 5.75 m² – 0.60
PATAMAR 4.00 m² – 0.16
RAMPA – i = 6.5%
RAMPA – i = 6.2%
ÁREA TÉCNICA 23.4 m² – 0.59
LAB. DE MOCKUP 121.85 m² – 0.59
HALL LAB. MOCKUP 2.3 m² + 0.59
LAB. DE FÍSICA E CARACTERIZAÇÃO ELETROMAGNÉTICA DE MATERIAIS 55.1 m² +0.595
LAB. DE FÍSICA E CARACTERIZAÇÃO ELETROMAGNÉTICA DE MATERIAIS 54.1 m² +0.595
LAB. DE ELETRICIDADE E ENERGIA 94.2 m² +0.595
LAB. DE MATERIAIS 54.75 m² +0.595
APOIO 6.45 m² +0.595
HALL DE ACESSO 51.1 m² +0.58
SALA DE APOIO 6.65 m² +0.595
LAB. DE QUÍMICA GERAL E ENERGIA 58.2 m² +0.595
ESTAR/COPA FUNCIONÁRIOS 48.6 m² +0.595

03	REVISÃO PASSEIOS - SAP 29	FABIANA	08/11/2011
02	COMPATIBILIZAÇÃO ARQUITETURA E ESTRUTURA - SAP 07	FABIANA	30/07/2010
01	REVISÃO DE LAYOUT	FABIANA	21/01/2010
REVISÃO Nº	ALTERAÇÃO	RESPONSÁVEL	DATA

Fundação Universidade de Brasília
Centro de Planejamento Oscar Niemeyer

FACULDADE UnB GAMA

UED - UNIDADE DE ENSINO E DOCÊNCIA
PROJETO - 04.01

PROJETO EXECUTIVO
ARQUITETURA

ESCALA: 1/100
UNIDADE: METROS
DATA: MAI/09
DESENHO: EQUIPE

PE-AR 02/ 36

COORD.: ARQ. ALBERTO DE FARIA

EQUIPE: ARQ. FABIANA COUTO
ARQ. FÁTIMA LAURIA PIRES

PLANTA BAIXA TÉRREO

X:\planejamento\CADASTRO SESU_MEC\gama\fga-ued-pe-ar-02-planta terreo 100-rev03 teste.dwg

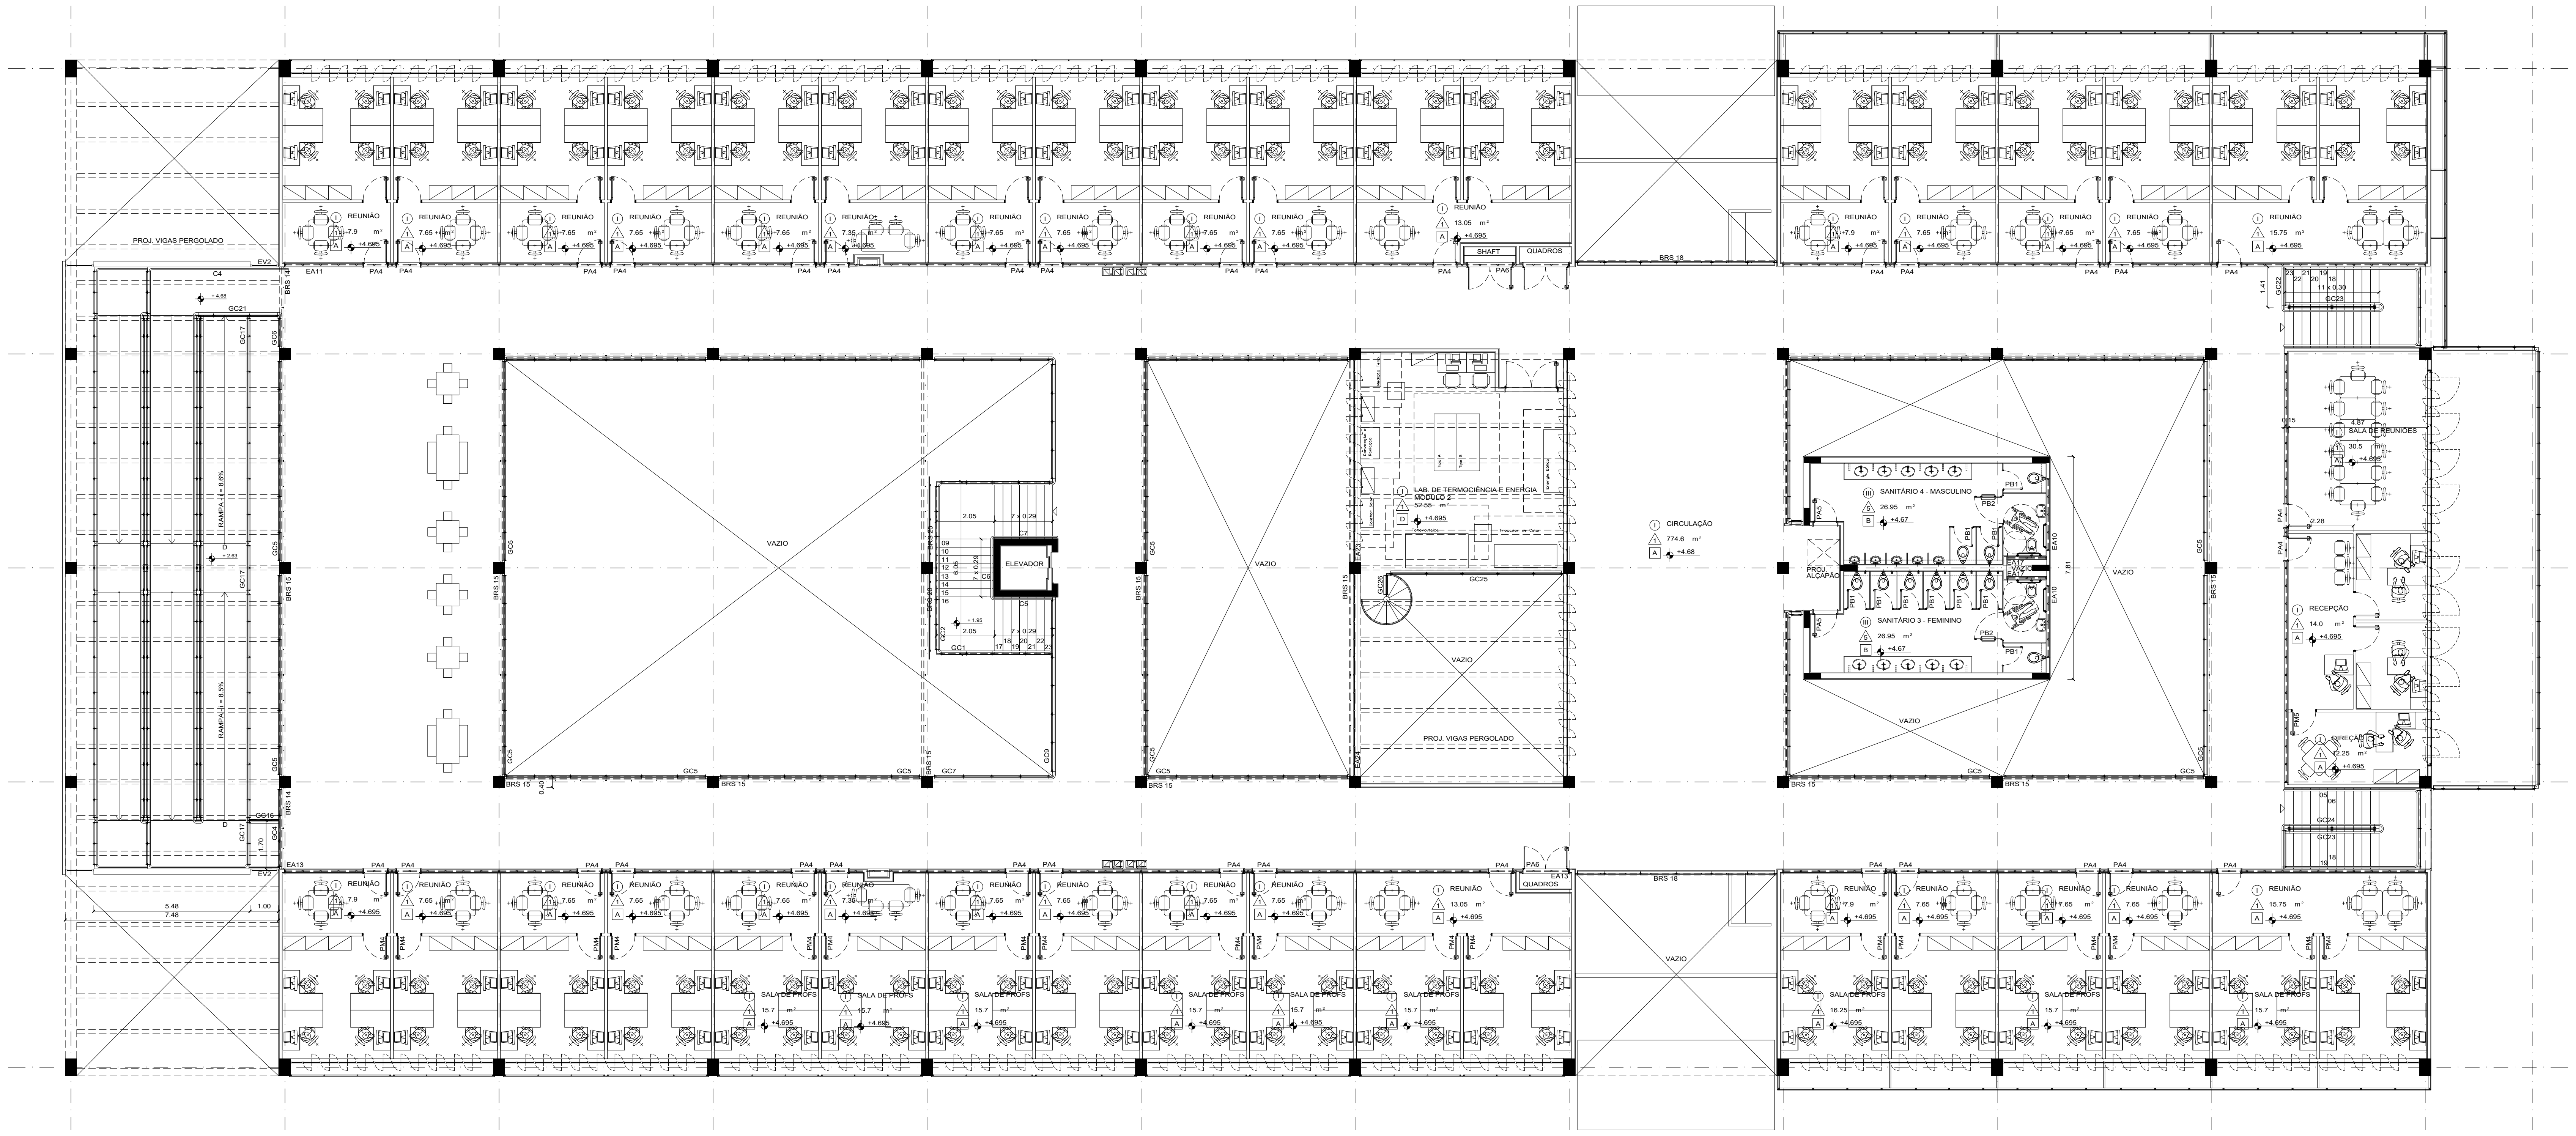

PLANTA PAVIMENTO SUPERIOR

1:100

ÁREA TOTAL DO PAVIMENTO
2.020 m²

REVISÃO Nº	ALTERAÇÃO	RESPONSÁVEL	DATA
02	COMPATIBILIZAÇÃO ARQUITETURA E ESTRUTURA - SAP 07	FABIANA	30/07/2010
01	REVISÃO LAYOUT	FABIANA	21/01/2010

Fundação Universidade de Brasília
Centro de Planejamento Oscar Niemeyer

FACULDADE UnB GAMA

UED - UNIDADE DE ENSINO E DOCÊNCIA
PROJETO - 04.01

PROJETO EXECUTIVO
ARQUITETURA

ESCALA: 1/100
UNIDADE: METROS
DATA: MAI/09
DESENHO: EQUIPE

PE-AR 03 / 36

COORD.: ARQ. ALBERTO DE FARIA

EQUIPE: ARQ. FABIANA COUTO
ARQ. FÁTIMA LAURIA PIRES

PLANTA BAIXA PAVIMENTO SUPERIOR

X:\planejamento\CADASTRO SESU_MEC\gama\fga-ued-pe-ar-03-planta superior 100-rev02 teste.dwg