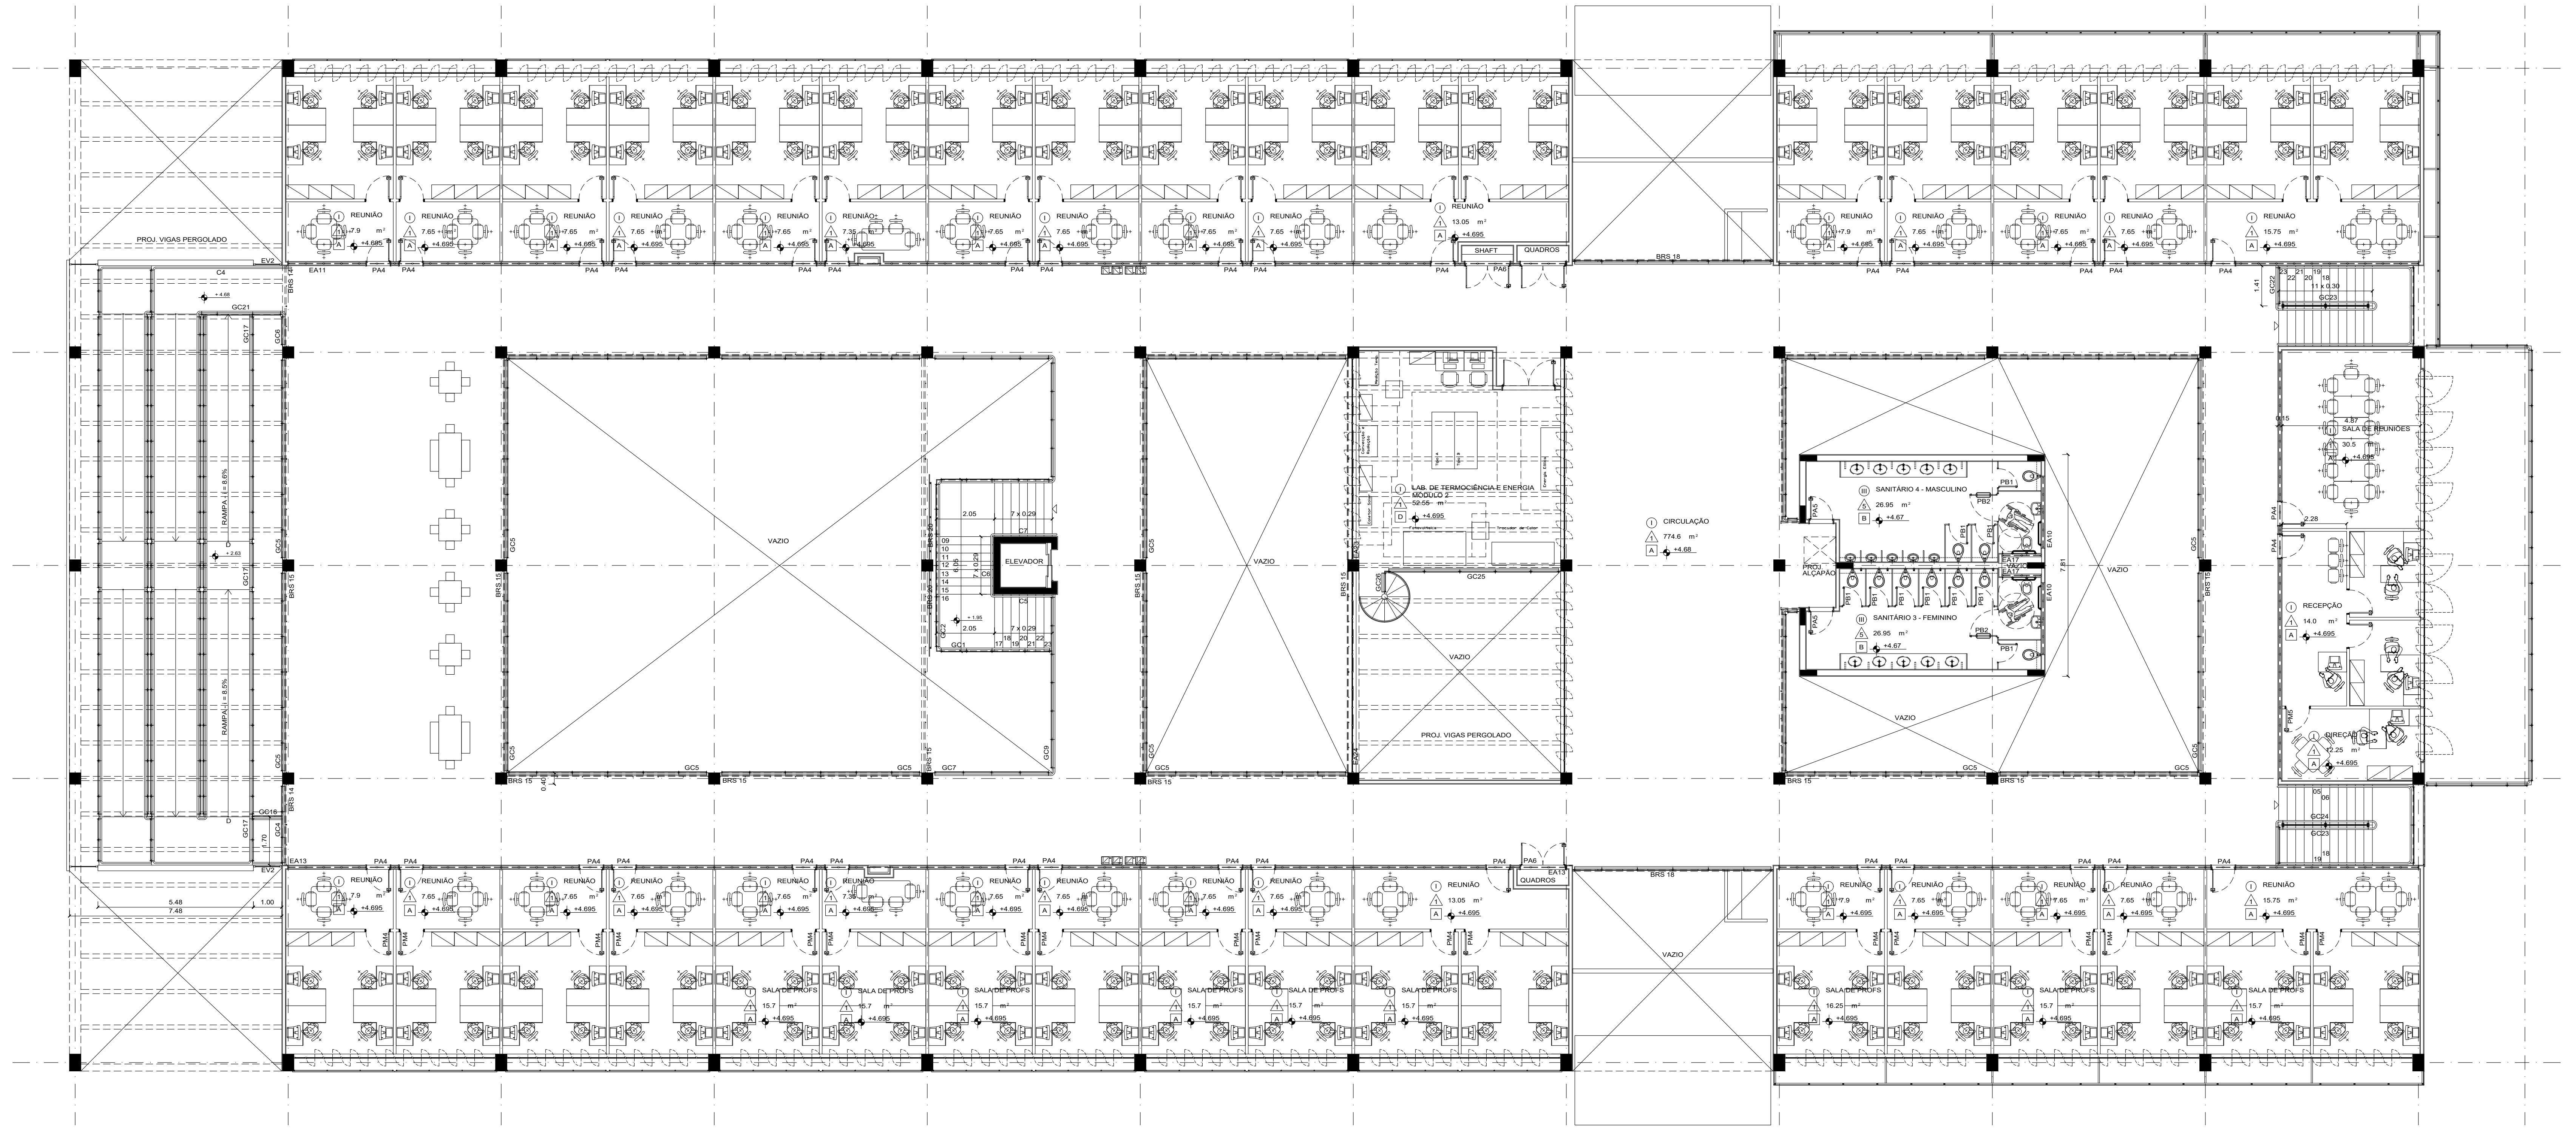

PLANTA PAVIMENTO SUPERIOR

1:100

ÁREA TOTAL DO PAVIMENTO
2.020 m²

REVISÃO Nº	ALTERAÇÃO	RESPONSÁVEL	DATA
02	COMPATIBILIZAÇÃO ARQUITETURA E ESTRUTURA - SAP 07	FABIANA	30/07/2010
01	REVISÃO LAYOUT	FABIANA	21/01/2010

Fundação Universidade de Brasília
Centro de Planejamento Oscar Niemeyer

FACULDADE UnB GAMA

UED - UNIDADE DE ENSINO E DOCÊNCIA
PROJETO - 04.01

PROJETO EXECUTIVO
ARQUITETURA

ESCALA: 1/100
UNIDADE: METROS
DATA: MAI/09
DESENHO: EQUIPE

PE-AR 03 / 36

COORD.: ARQ. ALBERTO DE FARIA

EQUIPE: ARQ. FABIANA COUTO
ARQ. FÁTIMA LAURIA PIRES

PLANTA BAIXA PAVIMENTO SUPERIOR

X:\planejamento\CADASTRO SESU_MEC\gama\fga-ued-pe-ar-03-planta superior 100-rev02 teste.dwg