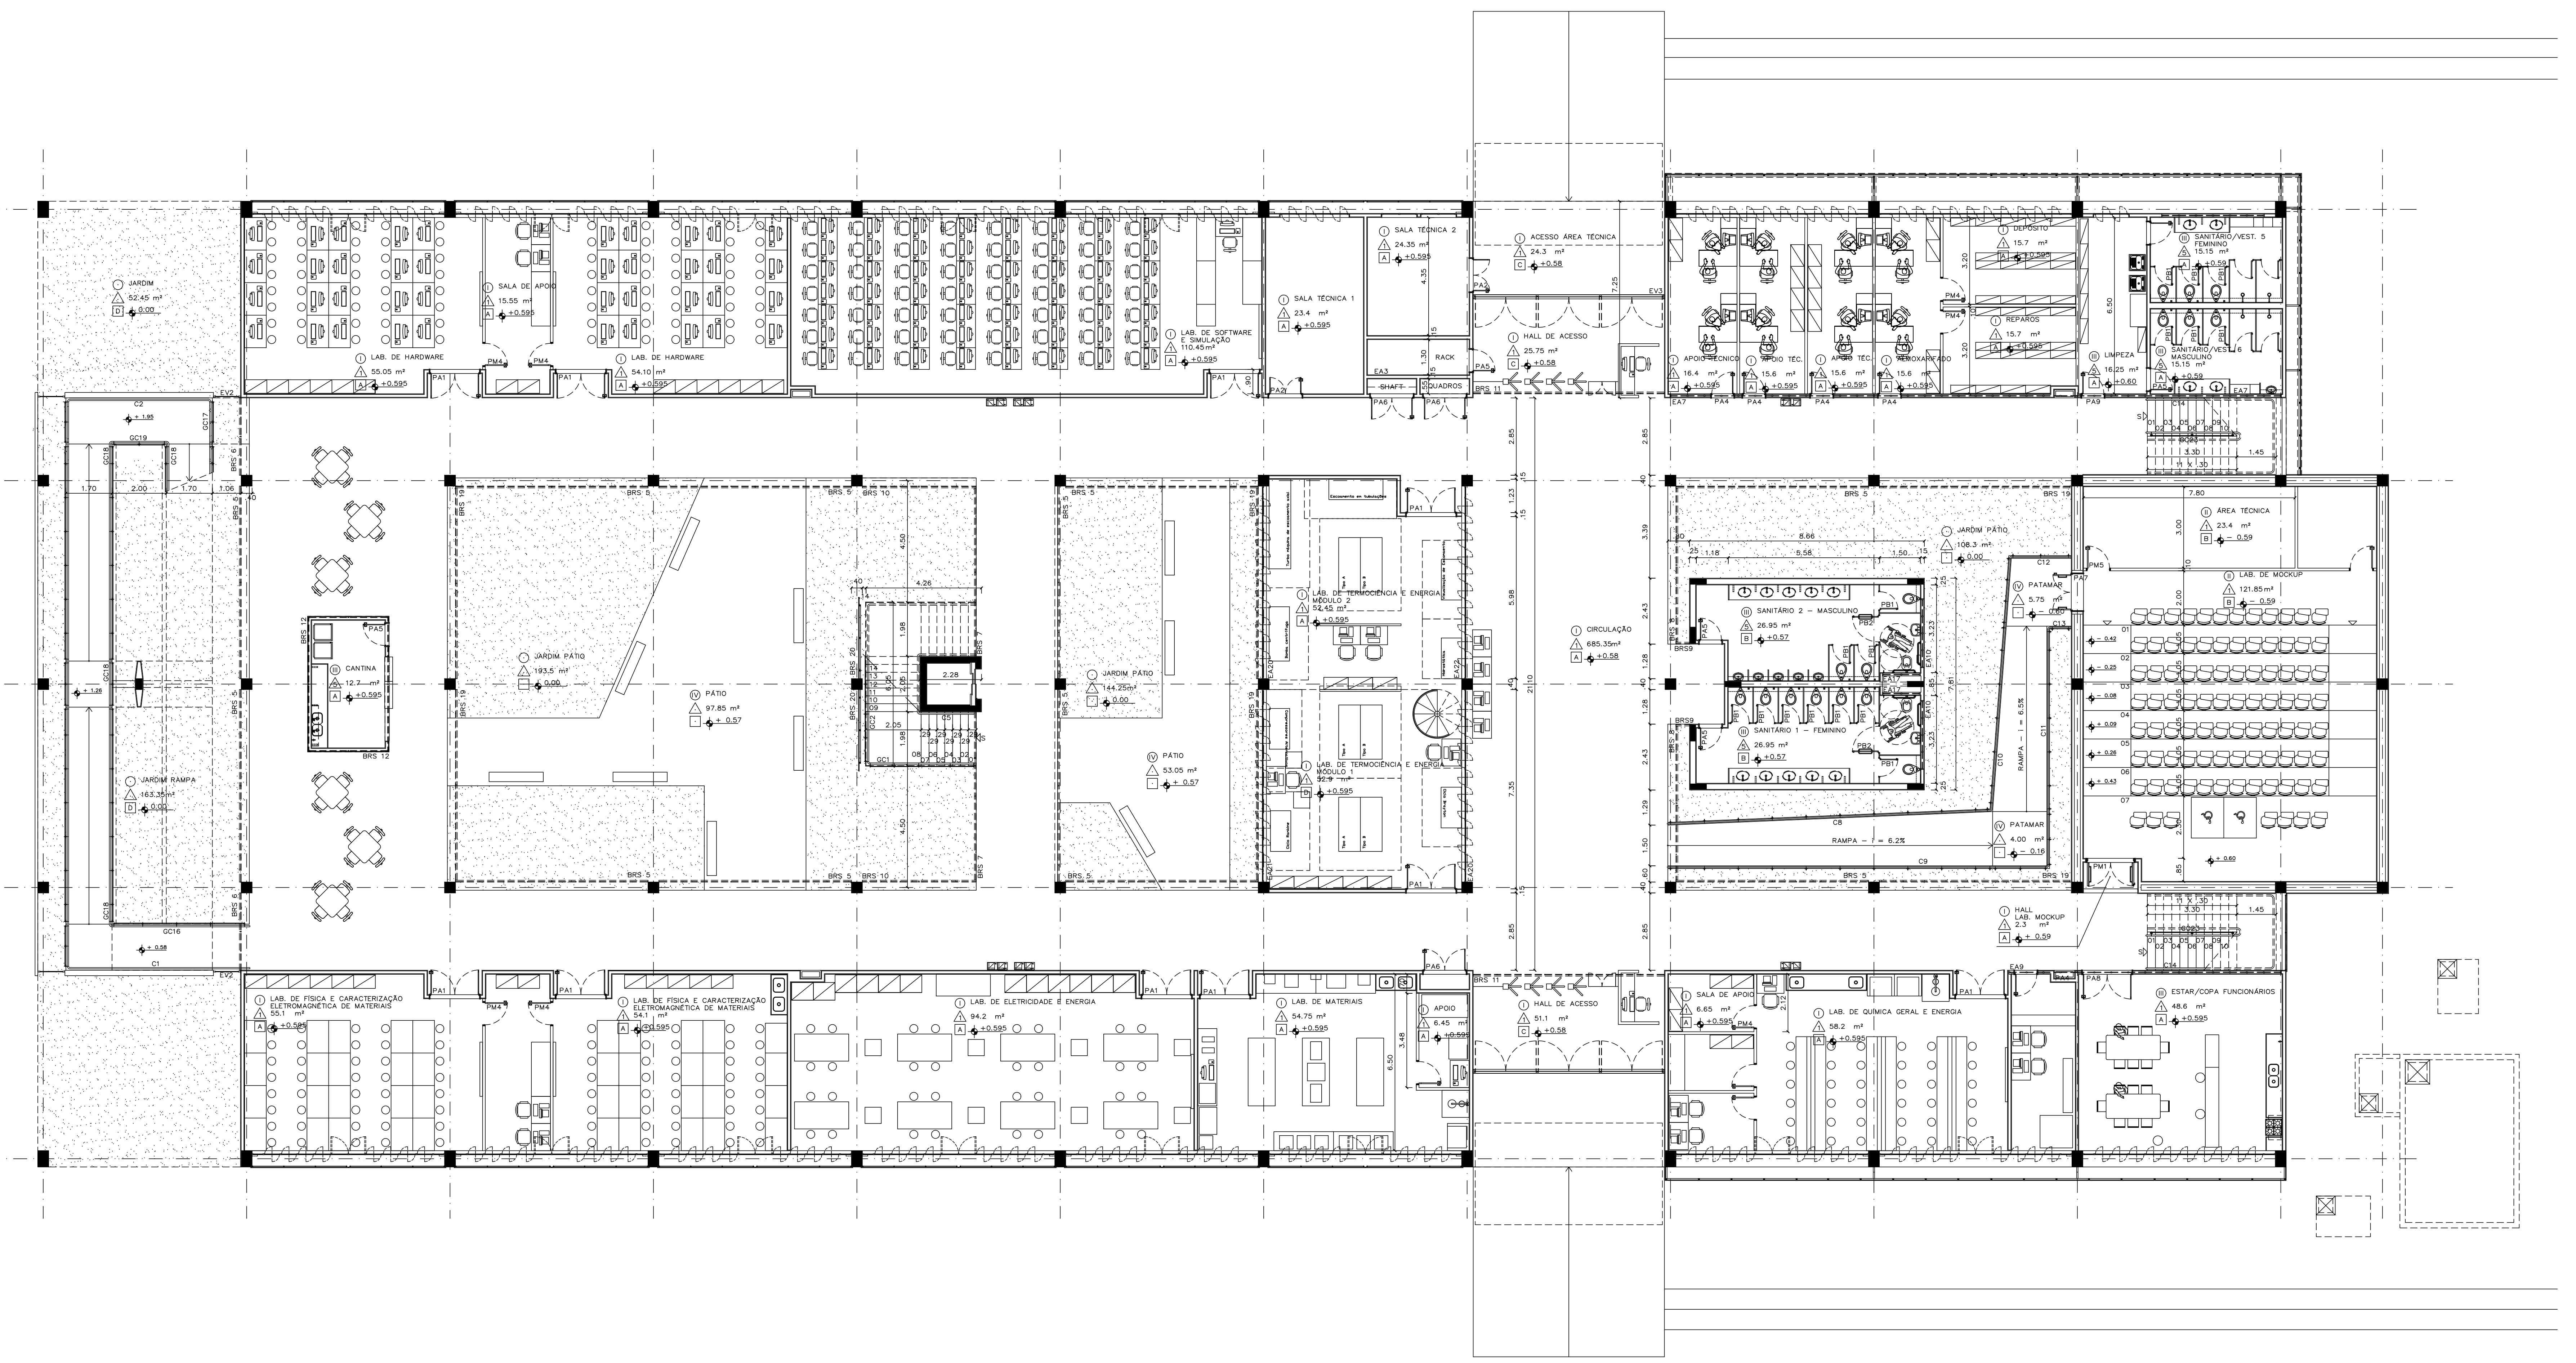

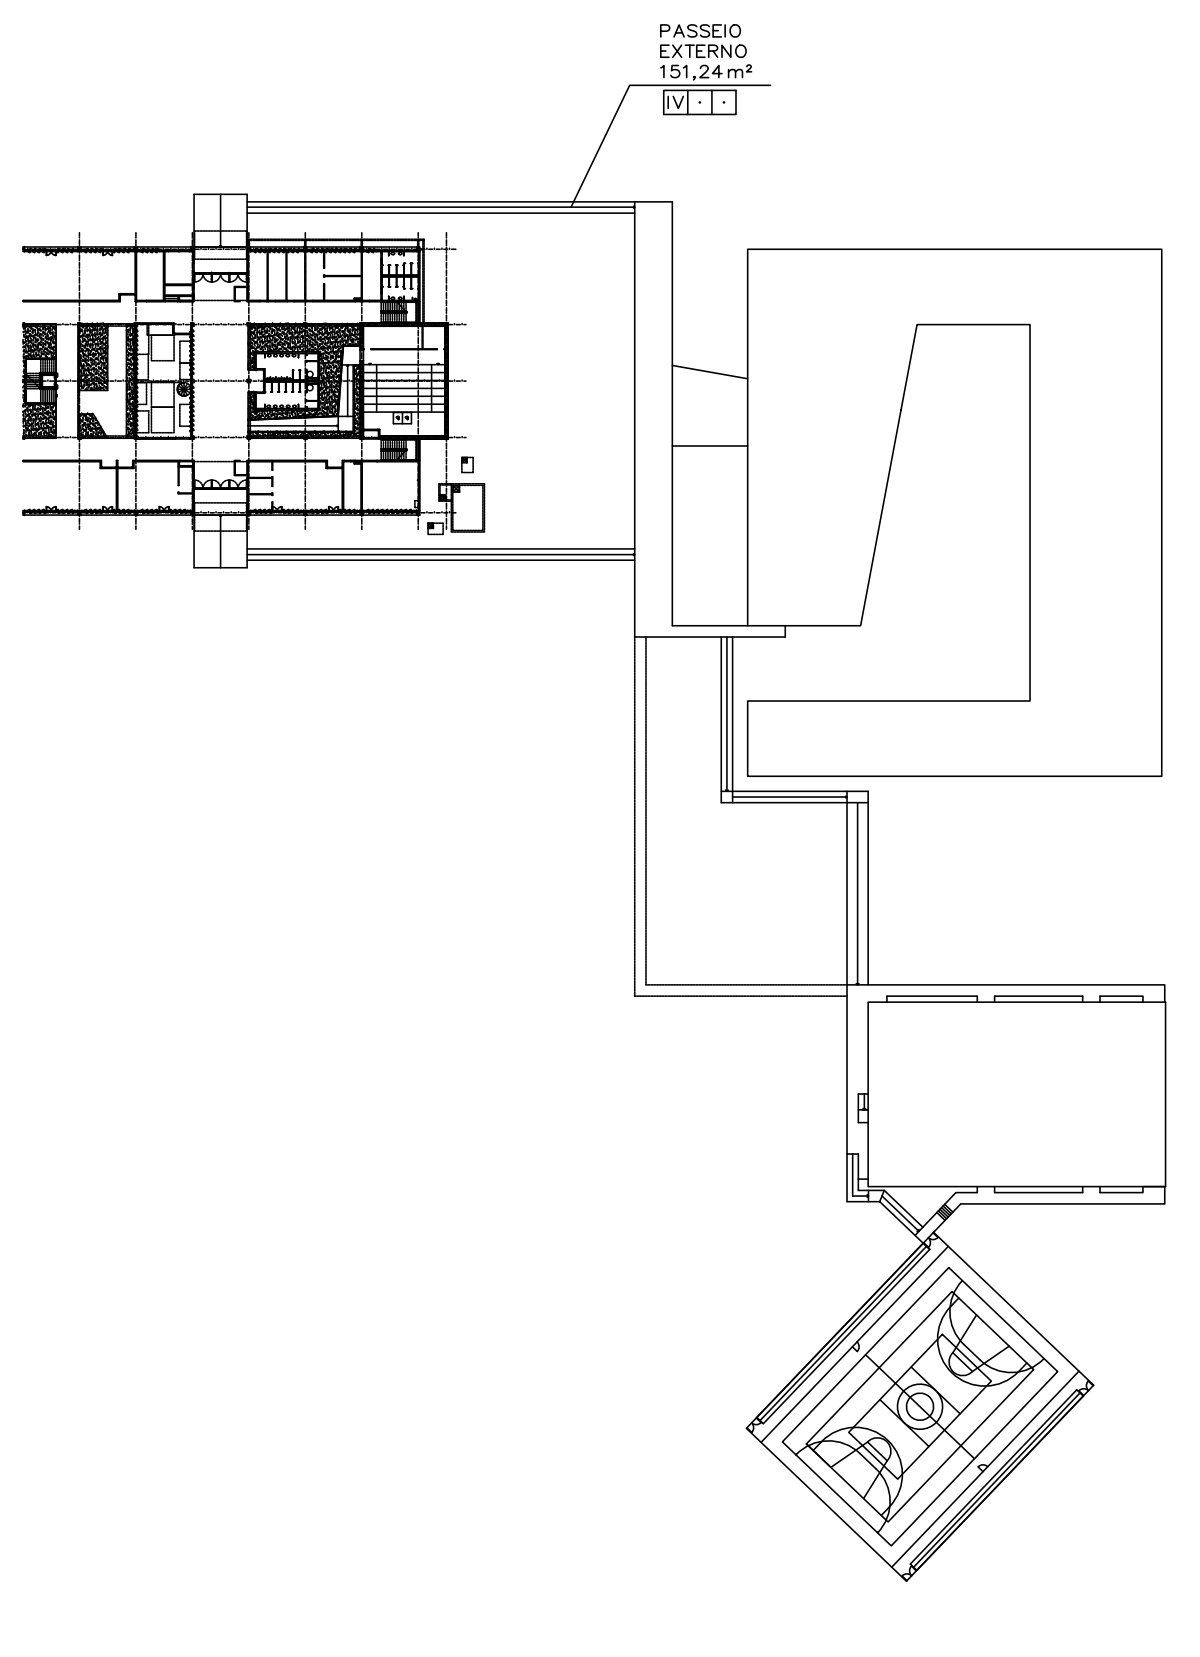

03	REVISÃO PASSEIOS - SAP 29	FABIANA	08/11/2011
02	COMPATIBILIZAÇÃO ARQUITETURA E ESTRUTURA - SAP 07	FABIANA	30/07/2010
01	REVISÃO DE LAYOUT	FABIANA	21/01/2010
REVISÃO Nº	ALTERAÇÃO	RESPONSÁVEL	DATA

Fundação Universidade de Brasília
Centro de Planejamento Oscar Niemeyer

FACULDADE UnB GAMA

UED - UNIDADE DE ENSINO E DOCÊNCIA
PROJETO - 04.01

PROJETO EXECUTIVO
ARQUITETURA

ESCALA: 1/100
UNIDADE: METROS
DATA: MAI/09
DESENHO: EQUIPE

PE-AR 02/ 36

COORD.: ARQ. ALBERTO DE FARIA

EQUIPE: ARQ. FABIANA COUTO
ARQ. FÁTIMA LAURIA PIRES

PLANTA BAIXA TÉRREO

X:\planejamento\CADASTRO SESU_MEC\gama\fga-ued-pe-ar-02-planta terreo 100-rev03 teste.dwg